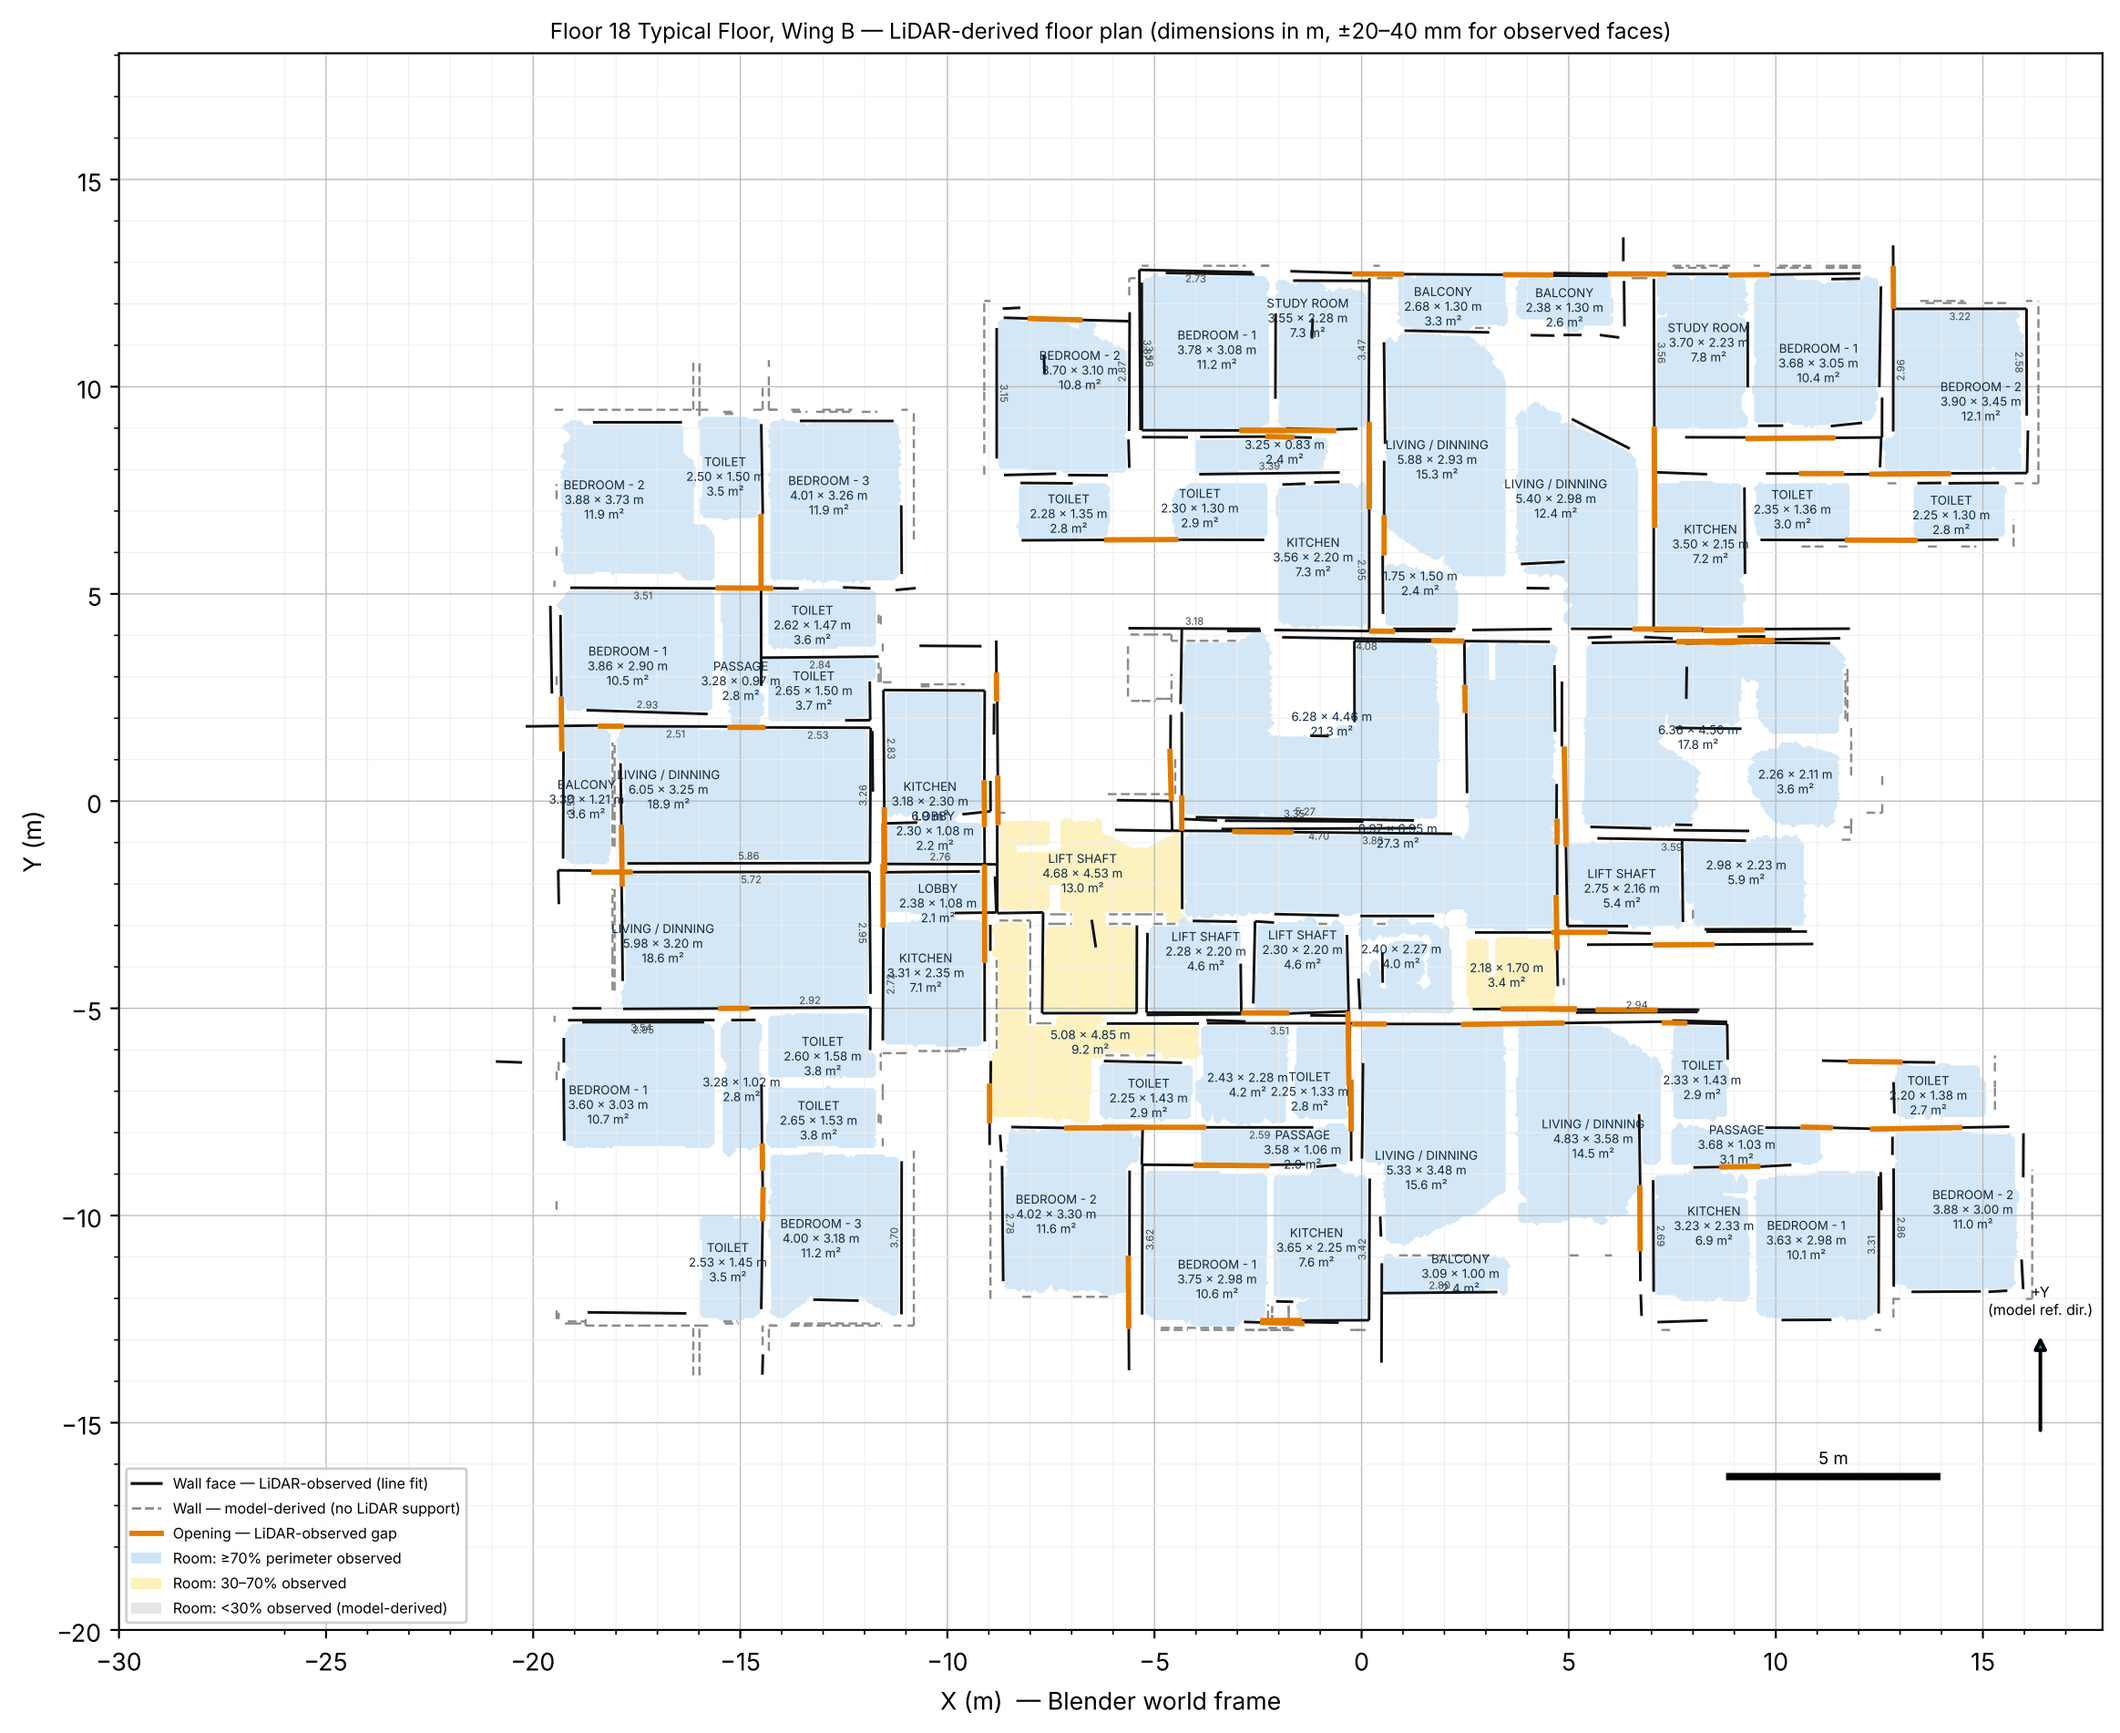

Floor 18 Typical Floor, Wing B — LiDAR-derived floor plan (dimensions in m, ±20–40 mm for observed faces)
BEDROOM - 2
3.88 × 3.73 m
11.9 m²
TOILET
2.50 × 1.50 m
3.5 m²
BEDROOM - 3
4.01 × 3.26 m
11.9 m²
BEDROOM - 1
3.86 × 2.90 m
10.5 m²
PASSAGE
3.28 × 0.97 m
2.8 m²
TOILET
2.62 × 1.47 m
3.6 m²
TOILET
2.65 × 1.50 m
3.7 m²
BALCONY
3.32 × 1.21 m
3.6 m²
LIVING / DINNING
6.05 × 3.25 m
18.9 m²
KITCHEN
3.18 × 2.30 m
7.0 m²
LOBBY
2.30 × 1.08 m
2.2 m²
LIVING / DINNING
5.98 × 3.20 m
18.6 m²
KITCHEN
3.31 × 2.35 m
7.1 m²
LOBBY
2.38 × 1.08 m
2.1 m²
BEDROOM - 1
3.60 × 3.03 m
10.7 m²
3.28 × 1.02 m
2.8 m²
TOILET
2.60 × 1.58 m
3.8 m²
TOILET
2.65 × 1.53 m
3.8 m²
TOILET
2.53 × 1.45 m
3.5 m²
BEDROOM - 3
4.00 × 3.18 m
11.2 m²
BEDROOM - 2
3.70 × 3.10 m
10.8 m²
BEDROOM - 1
3.78 × 3.08 m
11.2 m²
STUDY ROOM
3.55 × 2.28 m
7.3 m²
BALCONY
2.68 × 1.30 m
3.3 m²
BALCONY
2.38 × 1.30 m
2.6 m²
3.25 × 0.83 m
2.4 m²
TOILET
2.28 × 1.35 m
2.8 m²
TOILET
2.30 × 1.30 m
2.9 m²
KITCHEN
3.56 × 2.20 m
7.3 m²
LIVING / DINNING
5.88 × 2.93 m
15.3 m²
1.75 × 1.50 m
2.4 m²
LIVING / DINNING
5.40 × 2.98 m
12.4 m²
STUDY ROOM
3.70 × 2.23 m
7.8 m²
BEDROOM - 1
3.68 × 3.05 m
10.4 m²
KITCHEN
3.50 × 2.15 m
7.2 m²
TOILET
2.35 × 1.36 m
3.0 m²
TOILET
2.25 × 1.30 m
2.8 m²
BEDROOM - 2
3.90 × 3.45 m
12.1 m²
6.28 × 4.46 m
21.3 m²
6.36 × 4.56 m
17.8 m²
2.26 × 2.11 m
3.6 m²
LIFT SHAFT
4.68 × 4.53 m
13.0 m²
LIFT SHAFT
2.75 × 2.16 m
5.4 m²
2.98 × 2.23 m
5.9 m²
LIFT SHAFT
2.28 × 2.20 m
4.6 m²
LIFT SHAFT
2.30 × 2.20 m
4.6 m²
2.40 × 2.27 m
4.0 m²
2.18 × 1.70 m
3.4 m²
5.08 × 4.85 m
9.2 m²
TOILET
2.25 × 1.43 m
2.9 m²
2.43 × 2.28 m
4.2 m²
TOILET
2.25 × 1.33 m
2.8 m²
TOILET
2.33 × 1.43 m
2.9 m²
TOILET
2.20 × 1.38 m
2.7 m²
LIVING / DINNING
4.83 × 3.58 m
14.5 m²
PASSAGE
3.58 × 1.06 m
2.0 m²
PASSAGE
3.68 × 1.03 m
3.1 m²
LIVING / DINNING
5.33 × 3.48 m
15.6 m²
BEDROOM - 2
4.02 × 3.30 m
11.6 m²
BEDROOM - 1
3.75 × 2.98 m
10.6 m²
KITCHEN
3.65 × 2.25 m
7.6 m²
BALCONY
3.09 × 1.00 m
2.9 m²
KITCHEN
3.23 × 2.33 m
6.9 m²
BEDROOM - 1
3.63 × 2.98 m
10.1 m²
BEDROOM - 2
3.88 × 3.00 m
11.0 m²
+Y
(model ref. dir.)
5 m
Wall face — LiDAR-observed (line fit)
Wall — model-derived (no LiDAR support)
Opening — LiDAR-observed gap
Room: ≥70% perimeter observed
Room: 30–70% observed
Room: <30% observed (model-derived)
X (m) — Blender world frame
Y (m)
15
10
5
0
−5
−10
−15
−20
−30
−25
−20
−15
−10
−5
0
5
10
15